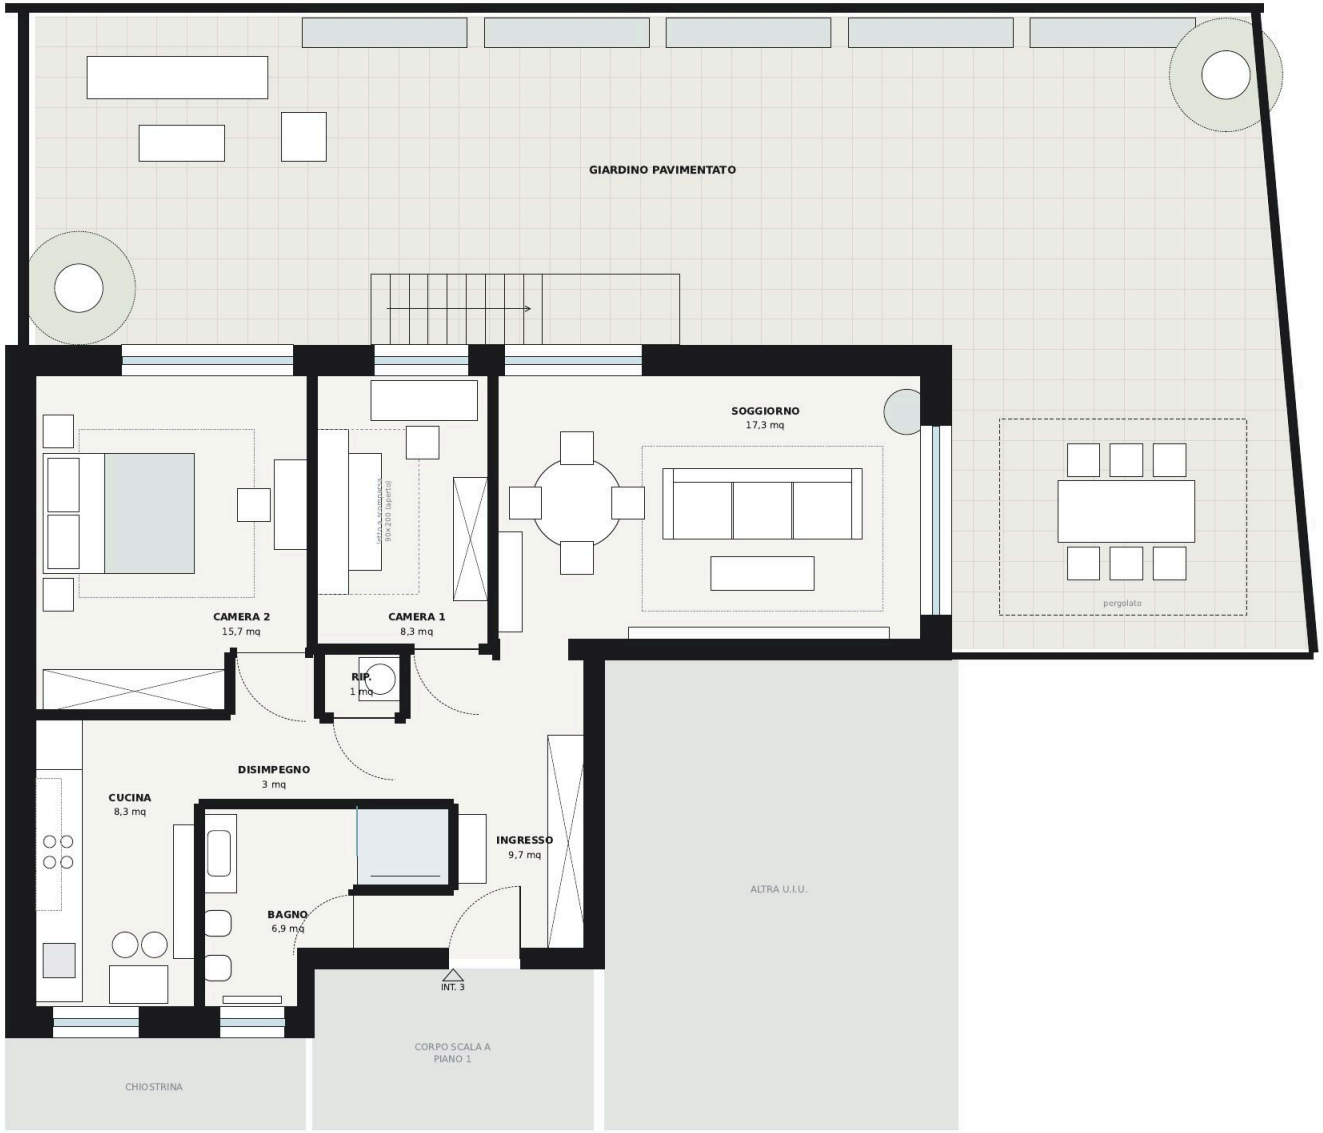


N

0 1 2 3 4 5

metri - scala 1:50 su A2

CASA SALVATORE

Studio d'arredo su base Tav. 02
Progetto definitivo del 03-07-2026

TAV. 01

Pianta arredata
Proposta

Ingresso trasformato in guardaroba: armadio 60 cm a tutta altezza e panca.

Ripostiglio usato come lavanderia (lavatrice e asciugatrice in colonna).

Camera 1 studio con letto a scomparsa 90×200, armadio da 45 cm.

Cucina lineare 3,70 m e dispensa da 35 cm: corridoio di lavoro 1,20 m.


Soggiorno con pranzo Ø 120 vicino alla porta-finestra e living verso la TV.

Giardino: pranzo sotto pergolato, zona relax a ovest, fioriere sul confine.

Scala 1:50 (formato A2)

Data 25-10-2026

Elaborato di studio: misure ricavate dalla scala grafica, da verificare con rilievo.

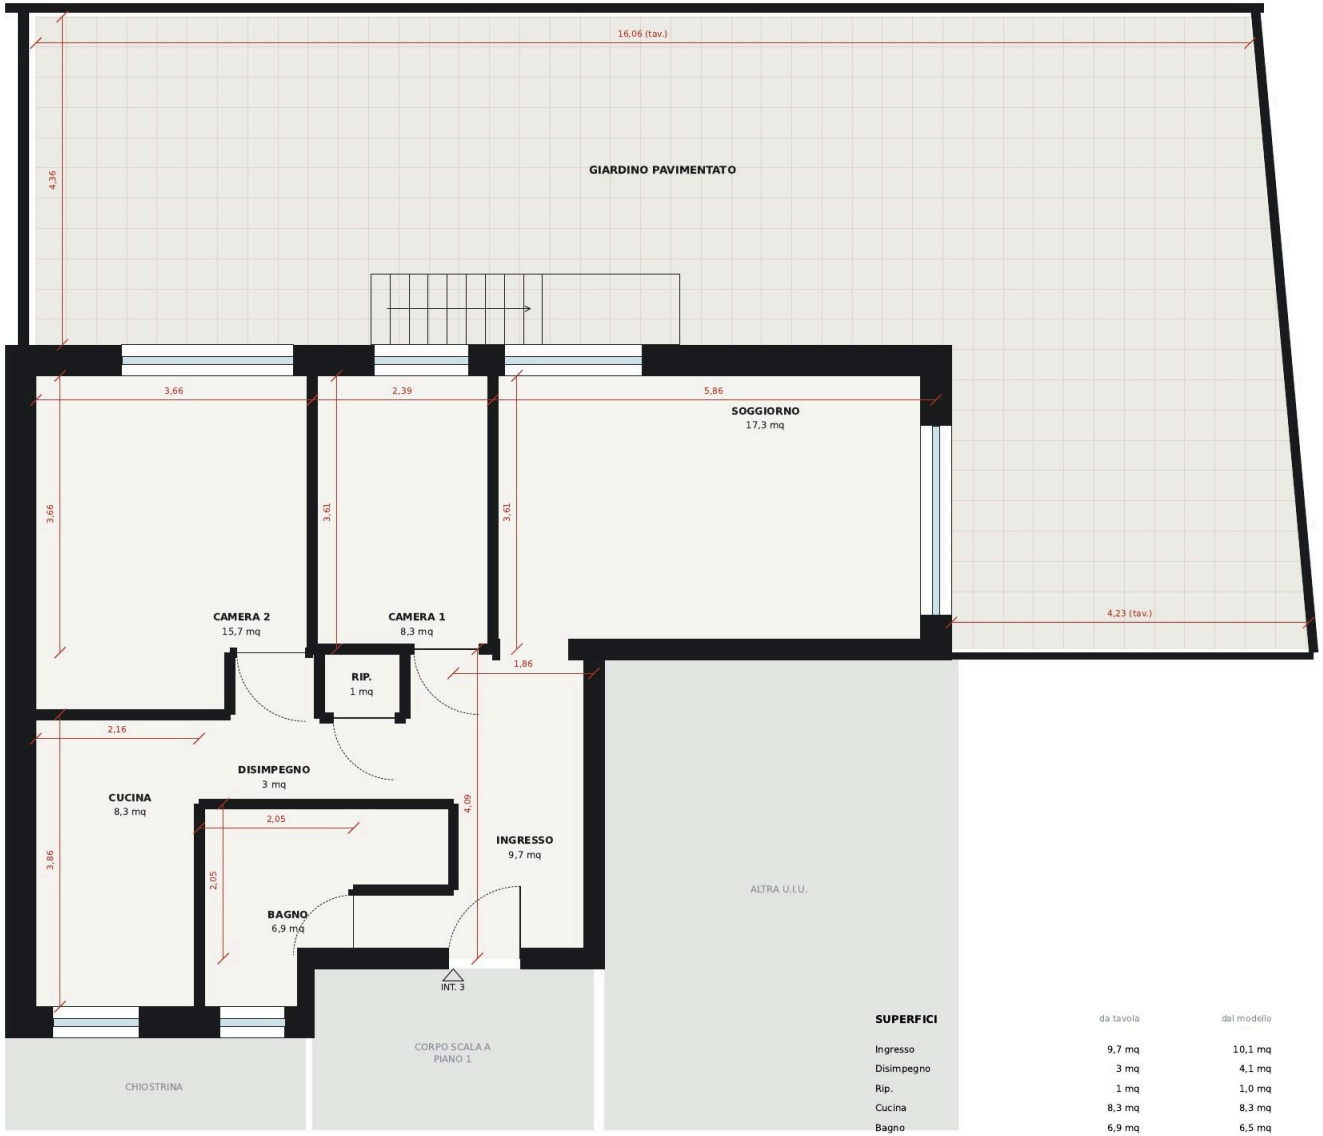

SUPERFICI	da tavola	dal modello
Ingresso	9,7 mq	10,1 mq
Disimpegno	3 mq	4,1 mq
Rip.	1 mq	1,0 mq
Cucina	8,3 mq	8,3 mq
Bagno	6,9 mq	6,5 mq
Camera 1	8,3 mq	8,6 mq
Camera 2	15,7 mq	15,5 mq
Soggiorno	17,3 mq	21,2 mq
Totale interno	**70,2 mq**	**75,4 mq**
Giardino	17,3 mq	89 mq

N

0 1 2 3 4 5

metri - scala 1:50 su A2

CASA SALVATORE

Studio d'arredo su base Tav. 02
Progetto definitivo del 03-07-2026

TAV. 02

Pianta quotata e superfici

Quote rosse in metri, misurate sul filo interno dei muri.

Le quote 16,06 e 4,23 sono riportate dalla Tav. 02 originale.

Altezza interna assunta 2,80 m: non indicata in tavola.

Dislivello della scala del giardino non quotato: da verificare.

Superficie del giardino: in tavola 17,3 mq, dal disegno risulta molto maggiore. Da verificare con il tecnico.

Scala 1:50 (formato A2)

Data 25-10-2026

Elaborato di studio: misure ricavate dalla scala grafica, da verificare con rilievo.



01 Assonometria da sud




03 Assonometria dal giardino




04 Soggiorno



05 Giardino verso il soggiorno

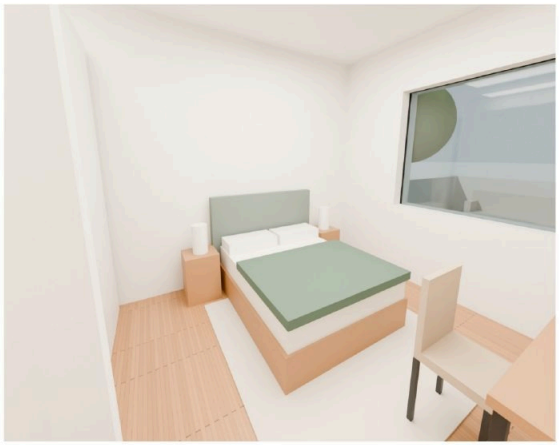

06 Camera 2

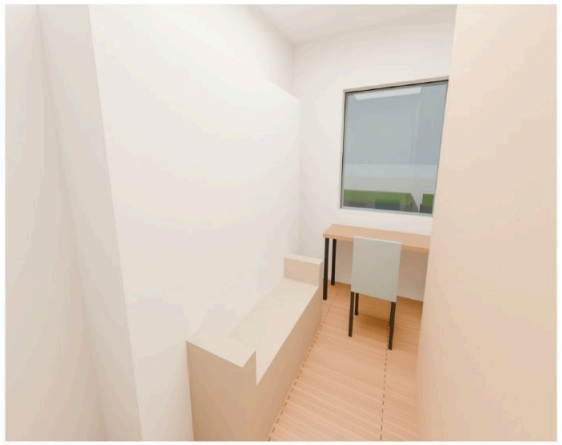


07 Camera 1



08 Cucina



09 Bagno

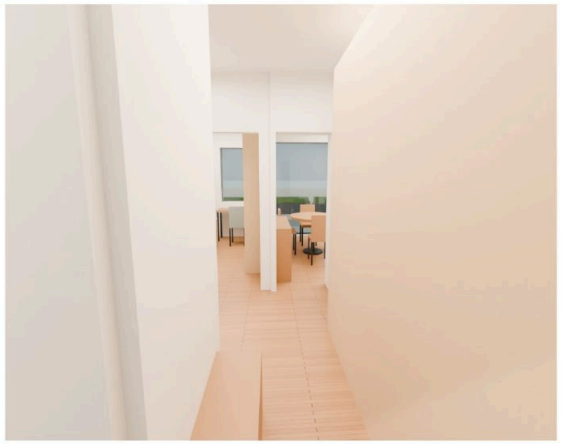

10 Ingresso

CASA SALVATORE

Studio d'arredo su base Tav. 02
Progetto definitivo del 03-07-2026

TAV. 03

Viste 3D della proposta

Rendering del modello con l'arredo proposto nelle tavole 01 e 02.

Materiali e colori indicativi: servono a leggere volumi e proporzioni, non sono scelte di finitura.

Scala 1:50 (formato A2)

Data 25-10-2026

Elaborato di studio: misure ricavate dalla scala grafica, da verificare con rilievo.